Ansicht
25
24
23
22
21
20
A - A
19
18
17
B - B
16
15
14
C - C
13
12
11
10
9
8
8.75
7.50
6.25
U
T
S
R
Q
P
O
N''
N
M
L
K
J
INTERMEDIATE CARE 2 (IMC) - 24 BETTEN
INTERMEDIATE CARE 1 (IMC) - 24 BETTEN
Freianlagen siehe Plan STP
ZENTRALESPATIENTENMANAGEMENT
HOF E00
E00 Intensive Begrünung
Ansicht Nord
Ansicht West
Neubau 1. BA
Bestand MKL
Schnitt 00-7
Zugang / Aufnahme Notambulanz
4.04.01.01 Foyer F 00.011 192.9 m²
4.04.01.06 Patientenaufnahme 6 Plätze F 00.001 37.0 m²
4.04.01.04 Warten Pat.-Aufnahme F 00.008 70.9 m²
Windfang Ebene 00 F 00.000 12.9 m²
Treppenraum F 00.020 23.7 m²
2.10.01.01 Behandlungszimmer 6 Plätze B 00.119 56.6 m²
2.10.02.01 Behandlungsstützpunkt B 00.118 29.9 m²
2.10.01.02 Behandlungszimmer 6 Plätze B 00.117 56.6 m²
FLur B 00.109 94.5 m²
Treppenhaus B 00.140 25.8 m²
2.10.01.11 Patientenaufenthalt B 00.139 23.3 m²
Pat.-Balkon B 00.109-B 9.0 m²

Allgemeines
- Alle Maße sind vor Baubeginn zu prüfen!
Unstimmigkeiten sind der Bauleitung umgehend mitzuteilen!
- Tür- sowie Brüstungshöhen beziehen sich auf FFB.
- Angabe der Abmessungen Unterzüge, Überzüge und Fundamente n.A. KKI
- Angaben zu AWT und Aufzügen n.A. MMG
- Angaben zu Lerrohren, Fundamet- Ringerder und Blitzschutz n.A. IBB
- Angaben zu Grundleitungen und TAD n.A. PBW
- Materialien siehe Überstichtspläne Wände, Decken, Böden und Türen
- Wandverstärkungen und Wandeinaufen s. Höhenrasterplan und Raumdetails
- Türangaben siehe Türliste

BKT (Betonkerntemperierung) - Module; s. Planung TAD n.A. PBW

Bohrverbotzone; s. Planung TAD n.A. PBW

Bodeneinlauf n.A. PBW

Materialien

Stahlbeton	Systemtrennwand	Verglasung F0
Beton	OP Systemtrennwand	Verglasung F30
Halbfertigteil, Elementwand	Gipskartonwand F0	Verglasung F90
Betonfertigteil	Gipskartonwand F0/F30	Dämmung druckfest
Mauerwerk	Gipskartonwand F30	Dämmung weich
Mauerwerk, nach Installation	Gipskartonwand F90	

Oberflächen
SB 2/3 ▷ Sichtbetonqualität SB2/3

Eckschutz
○ 2.26m ○ 2.50m ○ 3.00m ○ raumhoch

Zulagen
- GKI FL raumhoch
- GKI FL halbhoch 2.00m
- GKI FL halbhoch 1.40m
- ZBP FL raumhoch
- S fliesenbündig H:140cm
- S fliesenbündig H:80cm

Rammschutz
- Rh1-K=Rammschutz halbhoch 1.10m, Keramik
- Rh2-K=Rammschutz halbhoch 0.80m, Keramik
- Rh3-K=Rammschutz halbhoch 0.75m, Keramik
- Rh4-K=Rammschutz halbhoch 1.20m, Keramik
- Rt-DPL=Rammschutz türhoch, DPL
- Rr-DPL=Rammschutz raumhoch, DPL

Zulagen
- St = Strahlenschutz, 20cm IORT
- St = Strahlenschutz, 0.1mm
- St = Strahlenschutz, 0.5mm
- St = Strahlenschutz, 1.0mm
- St = Strahlenschutz, 1.5mm
- St = Strahlenschutz, 2.0mm
- St = Strahlenschutz, 2.5mm
- St = Strahlenschutz, 3.0mm

Schlitz- und Durchbruchsplanung Hinweis: "S+D TB unter 150 mm sind in den Plänen nicht dargestellt"

Alle Durchbruchsangaben in cm
Vermaßung in Architekturvermaßung
Der Bezug zur UKRD ist immer auf der Seite, auf der der Text steht

E Elektro	K Kälte	TGA Mehrere Gewerke	
FA Aufzüge	L Lüftung	WD Wanddurchbruch	
FR Rohrpost	S Sanitär	BD Bodendurchbruch	BS Bodenschlitz
G Medizinische Gase	SF Feuerlösch / Sprinkler	DD Deckendurchbruch	RH Rohrhülse
H Heizung	SPE Prov. Entwässerung	WS Wandschlitz	KB Kernbohrung senkrecht
HDA Dampf	SVE Sanitär VE Wasser	DS Deckenschlitz	RH Kernbohrung waagerecht

Brandschutz

	Brandwand	RST	Rauchschutztür	T90-RS	Tür der Feuerwiderstandsklasse T90 mit Rauchschutzfunktion nach DIN 18095
NA	Notausstieg	T30	Tür der Feuerwiderstandsklasse T30	dss	Tür dicht- und selbstschließend
RA	Rauchabzug	T30-RS	Tür der Feuerwiderstandsklasse T30 mit Rauchschutzfunktion nach DIN 18095		
MRA	Maschinelle Entrauchung				
WH	Wandhydrant	T90	Tür der Feuerwiderstandsklasse T90		
F	Feuerlöscher				

Symbole, Tür- und Raumstempel
- ▽ Fertigmaße
- ▼ Rohmaße

6420.98.106.01 Türnummer
T30-RS Brandschutzanforderung
HPL Material

6420.98.106	Raumnummer
C.5.05.1	Raumprogrammnummer
Gerätepflege	Raumbezeichnung
76..16m²	Fläche
LiRH 2.75m	lichte Raumhöhe
FB KAU	Bodenbelag
AD MIPLA	Deckenbekleidung
W GK	Wandbekleidung

Raumdetailverweis
⊗ AA5DGRAU022
Höhenkoten Decke
UKRD= -0.36
UKAD= -2.28
Höhenkoten Fußboden
FFB +/-0.00
RFB -0.15

Allgemeine Abkürzungen

AD	Abhangdecke	ET	Einbauteil	RH	Rohrhülse
AK	Außenkante	FFB	Fertigfußboden	RS	Rohrsohle
AS	Anschlagschiene	i.L.	im Lichten	RW	Regenwasser
BE	Bodeneinlauf	Li RH	lichte Raumhöhe	SW	Schmutzwasser
BP	Bodenplatte	MÖ	Montageöffnung	TS	Trennschiene
BR	Brüstung	MW	Mauerwerk	UD	abgehängte Decke/Unterdecke ab FFB
BRH	Brüstungshöhe über FFB	n.A.	nach Angabe	UK	Unterkante
DF	Dehnfuge	OK	Oberkante	UKD	Unterkante Decke
DKM	Druckknopfmelder	OL	Oberlicht	UK UZ	Unterkante Unterzug über FFB
DN	Durchmesser	RA	Rohrachse	UZ	Unterzug
DS	Deckenschott	RD	Rohdecke	VM	Vormauerung
		RFB	Rohfußboden	VK	Vorderkante

Bodenbeläge Abkürzungen

BES-AUS	Beschichtung staubbindend
BES-AWT	Beschichtung Außenbereich
BES-HLP	Beschichtung HLP
BES-NAS	Beschichtung Sanitärräume
BES-TGA	Beschichtung Technikräume
BWS	Betonwerkstein
FL	Fliesen
GR	Gitterrost
HKS	Hohlkehlsockel
KAU	Kautschuk
KAU Abl.	Kautschuk ableitfähig
LÜKA	Lüftungskanal System
PAR	Parkett
PVC	PVC
Saub.	Sauberlaufmatte
SO	Sonderkonstruktion z.B Bodenblech
TR	Terrazzo

Deckenbeläge Abkürzungen

A	Akustik
AN	Anstrich
D	Deckensegel
GK	Gipskarton Decken
GKI	Feuchtraumplatte
HK	Heiz-/Kühldecke
LÜKA	Lüftungskanal System
ME	Revisionsdecken Metall
MEFA	Metalldecke außen
MIPLA	Mineralfaser Akustikdecke
SP	Spachtelung mit Anstrich
SP/ME	Decke Fertignasszellen
WÄDÄ	Dämmung
ZBP	Zementbauplatte

Wandbeläge Abkürzungen

AN	Anstrich
BES-NAS	Beschichtung Sanitärräume
GK	Gipskarton, Vlies und Anstrich
GKI	Feuchtraumplatte
LÜKA	Lüftungskanal System
HPL	OP Systemwand HPL
SP	Spachtelung mit Anstrich
ZBP	Zementgebundeneplatte
HL	Handlauf
S	Spiegel
ST	Strahlenschutz
Pb	Blei
PbGW	Blei-Gleichwert

Ausstattung/Einbauten
- Baukonstruktive Einbauten (KG 370)
- Medizin- und labortechnische Anlagen (KG 474), Ausstattung (KG 610)
- Sanitärobjekte (KG 410), Heizkörper
- Schaltschränke (KG 440, KG 450)
- Förderanlagen (KG 460), Küchenanlagen (KG 470)
- Medientechnik (KG 610)

Ausbau Abkürzungen

GTS	Geräteträgerschiene (s. Höhenrasterplan)
W 101	Wandtyp (s.Wandlegende)
WV...	Wandverstärkung (s. Höhenrasterplan)

Index	Datum	Änderungsbeschreibung	Bearbeiter
IN20			
IN19	20.12.17	Trockenbau-Anschluss an MKL; Positoinen Räume LS Ambulanz + RIZ geändert; Vorsatzschalen AWT-Aufzüge angepasst; Umkleidekabine Flur Tagesklinik ergänzt	tr/ri
IN18	12.04.17	Bodenabläufe angepasst	hch/ri
IN17	28.11.16	WV für Bettvorhang BT E und BT F weggefallen, Raum ESWL angepasst	hch
IN16	26.10.16	Wandverstärkung für Bettvorhang BT E und BT F ergänzt	hch
IN15	21.10.16	Anpassung Ausführungsplanung Radiologische Großgeräte/ M3 Cyriax ergänzt, Brüstungen in BT A an Angabe KKI angepasst	rpt/ek
IN14	04.07.16	Spiegel ergänzt, Anpassung Ausführungsplanung Radiologische Großgeräte	rpt/ek
IN13	21.06.16	Rammschutz, Position von Monitor, VK in BT C, Innenhof FassadeTür angepasst, AWT1 Türe neu, Türschwelle Hörsaal ergänzt	rpt/hch
IN12	19.05.16	Neue Stand OPB eingelesen (13.05.2016); BT E Deckenverkofferung geändert, WV angepasst; Brüstungskanäle und Bodentanks n.A. IBB; BT F Deckenverkofferung und Montage Nische ergänzt	rpt/hch
IN11	12.05.16	BT E Wandstärke,WC Bes.Beh.,Türöffnung Pat.Zi., Montage Nische, WV, Deckenverkofferung nach Details ergänzt und angepasst	rpt/hch

AA5G G-00 101119

Planung
TIEMANN-PETRI UND PARTNER
FREIE ARCHITEKTEN BDA
www.tiemann-petri-und-partner.de

Tiemann-Petri und Partner Freie Architekten BDA
Am Hohengeren 1
70188 Stuttgart
Tel: 0711-6203099-0 Fax: 0711-6203099-20
E-Mail: projekt.heidelberg@tiemann-petri-und-partner.de

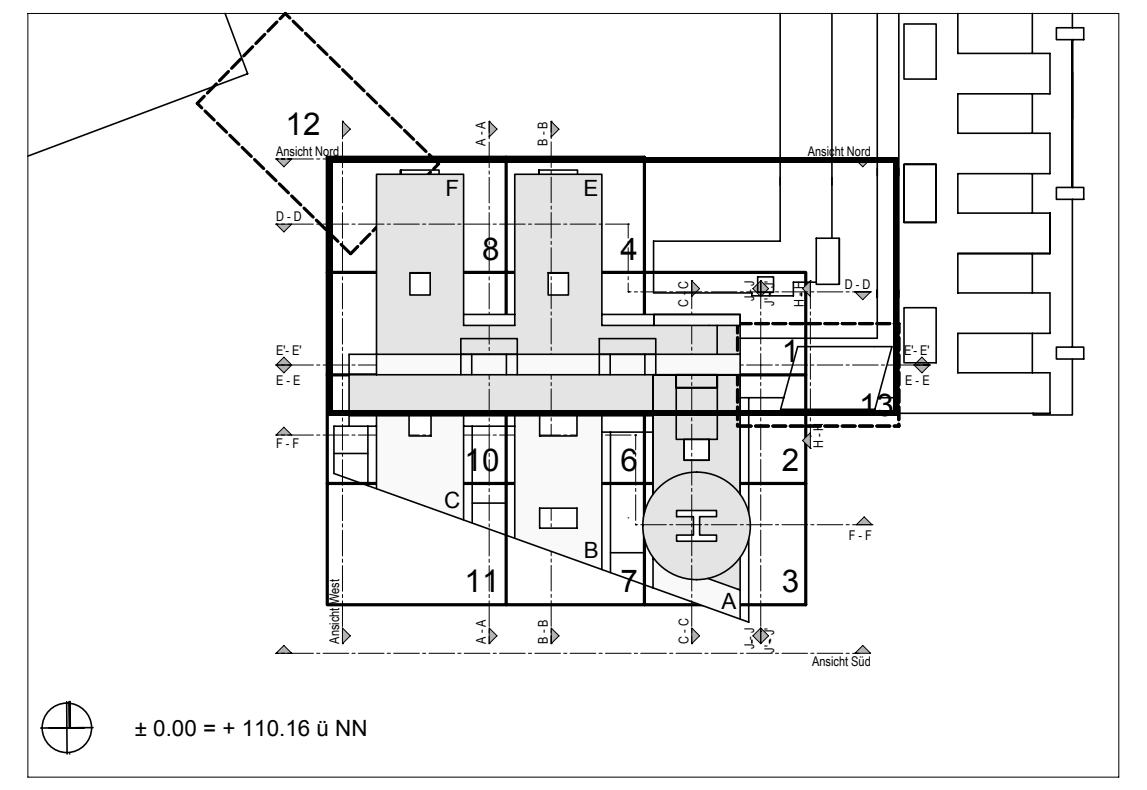
12
Ansicht Nord
A-A
B-B
D-D
F
E
8
4
1
E-E
F-F
10
6
2
C
B
A
11
7
3
13
Ansicht Süd
Ansicht West

± 0.00 = + 110.16 ü NN

Projekt Nr.
0004398700000001
SAP-WE SAP-Geb Nr.
Dienststelle 8211
Bauwerk 10006420
Nutzer Geb. Nr 6420
Dateiname AA5G G-00 101119.dwg
Dateiname XREF
F-5G G+00 000105
M3 E00 OPB Cyriax: 161014 M3
XRef3
XRef4
XRef5
Layoutname/Plancode AA5G G-00 101119
Plandatum 09.05.2014
Maßstab 1:100
Plangröße in mm 2070 X 900
Verfilmt am

Bauherr
Vermögen und Bau Baden-Württemberg
Universitätsbauamt Heidelberg
Im Neuenheimer Feld 100
69120 Heidelberg
Tel: 06221 – 546900 Fax: 06221 – 544399
E-Mail: poststelle.ubahd@vbv.bwl.de

Projekt
NB Chirurgische Universitätsklinik Heidelberg 1.BA
69120 Heidelberg
Im Neuenheimer Feld 420

Maßnahme
Neubau

Planbezeichnung
Bauabschnitt 1
Ausführungsplanung W4 Teil 1

Grundriss E 00

101119

Gezeichnet hch
Plan gesehen Unterschrift
Leiter des Amtes/Abteilungsl.
Bearbeiter hch